
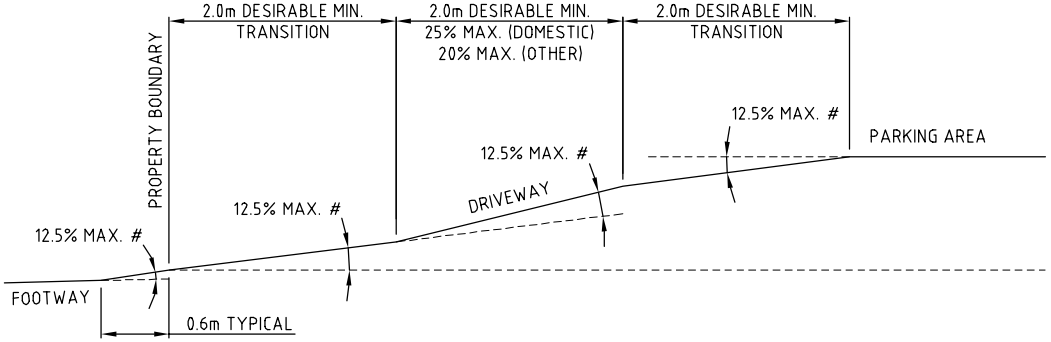


HIGH LEVEL PARKING DRIVEWAY PROFILE LIMITS

SCALE : NTS

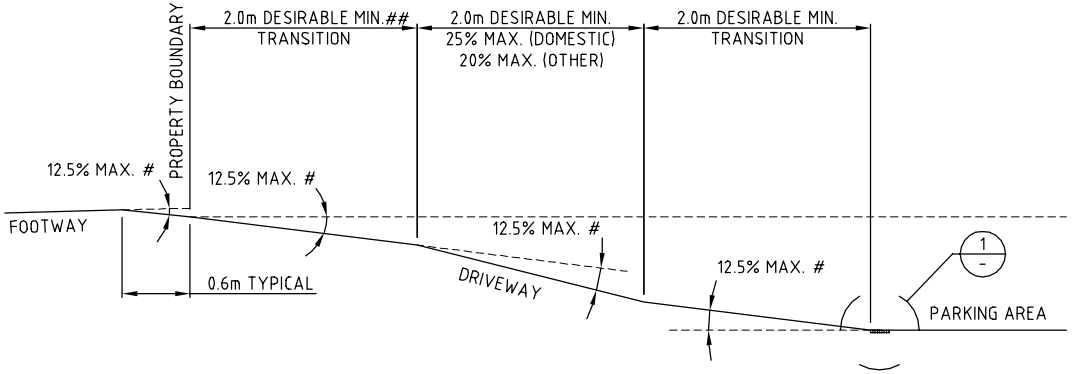

LOW LEVEL PARKING DRIVEWAY PROFILE LIMITS

SCALE : NTS

#. REFER TO NOTE 3.
##. REFER TO NOTE 9.

NOTES

1 THE DESIGN ENGINEER IS RESPONSIBLE FOR ENSURING THAT VEHICLES CAN TRAVERSE DRIVEWAYS WITHOUT SCRAPING IN COMPLIANCE WITH THIS GUIDE AND AS/NZ 2890.1

2 MAXIMUM GRADES SHOULD ONLY BE USED IN EXCEPTIONAL CIRCUMSTANCES. ON CURVED DRIVEWAYS THE MAXIMUM GRADES APPLY ON THE INSIDE OF THE CURVE.

3 THE MAXIMUM CHANGE OF GRADE AT ANY POINT IS NOT TO EXCEED 12.5%. ADDITIONAL TRANSITIONS OF 2M MINIMUM LENGTH CAN BE ADDED AS REQUIRED.

4 FOR FOOTWAY VEHICULAR CROSSING GRADES AND LEVEL GUIDELINES REFER TO B.C.C. STD DWG NO. S-028.


5 STREET BOUNDARY ALIGNMENT LEVELS AS OBTAINED FROM COUNCIL ARE TO BE INCORPORATED INTO DRIVEWAY PROFILE DESIGNS.

6 GRADES ARE DERIVED USING B.C.C. STD DWG NO. S-006 PASSENGER CAR CLEARANCE PROFILE. COMMERCIAL DEVELOPMENTS ARE TO USE THE B99 VEHICLE IN AS/NZS 2890.1

7 SPECIAL CONSIDERATION IS REQUIRED TO ALLOW "NON-STANDARD" AND "MODIFIED" VEHICLES TO CROSS WITHOUT SCRAPING WHERE REQUIRED. E.G. A STANDARD VEHICLE MODIFIED WITH A TOW BAR.

8. GRADES SHOWN ARE NOT APPLICABLE WHERE THE DISTANCE BETWEEN THE PROPERTY BOUNDARY AND THE GARAGE FLOOR IS LESS THAN 6.0m. REFER TO DESIGN ENGINEER FOR A SITE SPECIFIC DESIGN.

9. FOR UNIT/COMMERCIAL DEVELOPMENTS, PROVIDE 5% MAX. GRADE FOR 6.0m MIN. FROM THE PROPERTY BOUNDARY TO THE FIRST 2.0m MIN. TRANSITION IF REQUIRED.

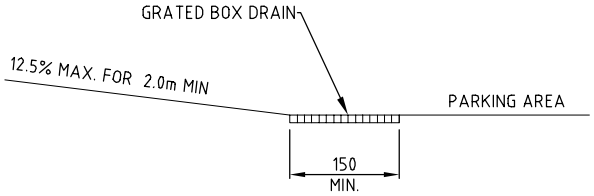

DETAIL 1 / -

SCALE : NTS

ALL DIMENSIONS ARE IN MILLIMETRES UNLESS NOTED OTHERWISE

CANTERBURY BANKSTOWN

CITY OF CANTERBURY BANKSTOWN

DRIVEWAY PROFILE GUIDELINES

HIGH AND LOW LEVEL PROFILES

STD DWG N°: S-005

Sheet N°: 1 of 1

Revision: 1/05/17

File Name: S-005.dwg